

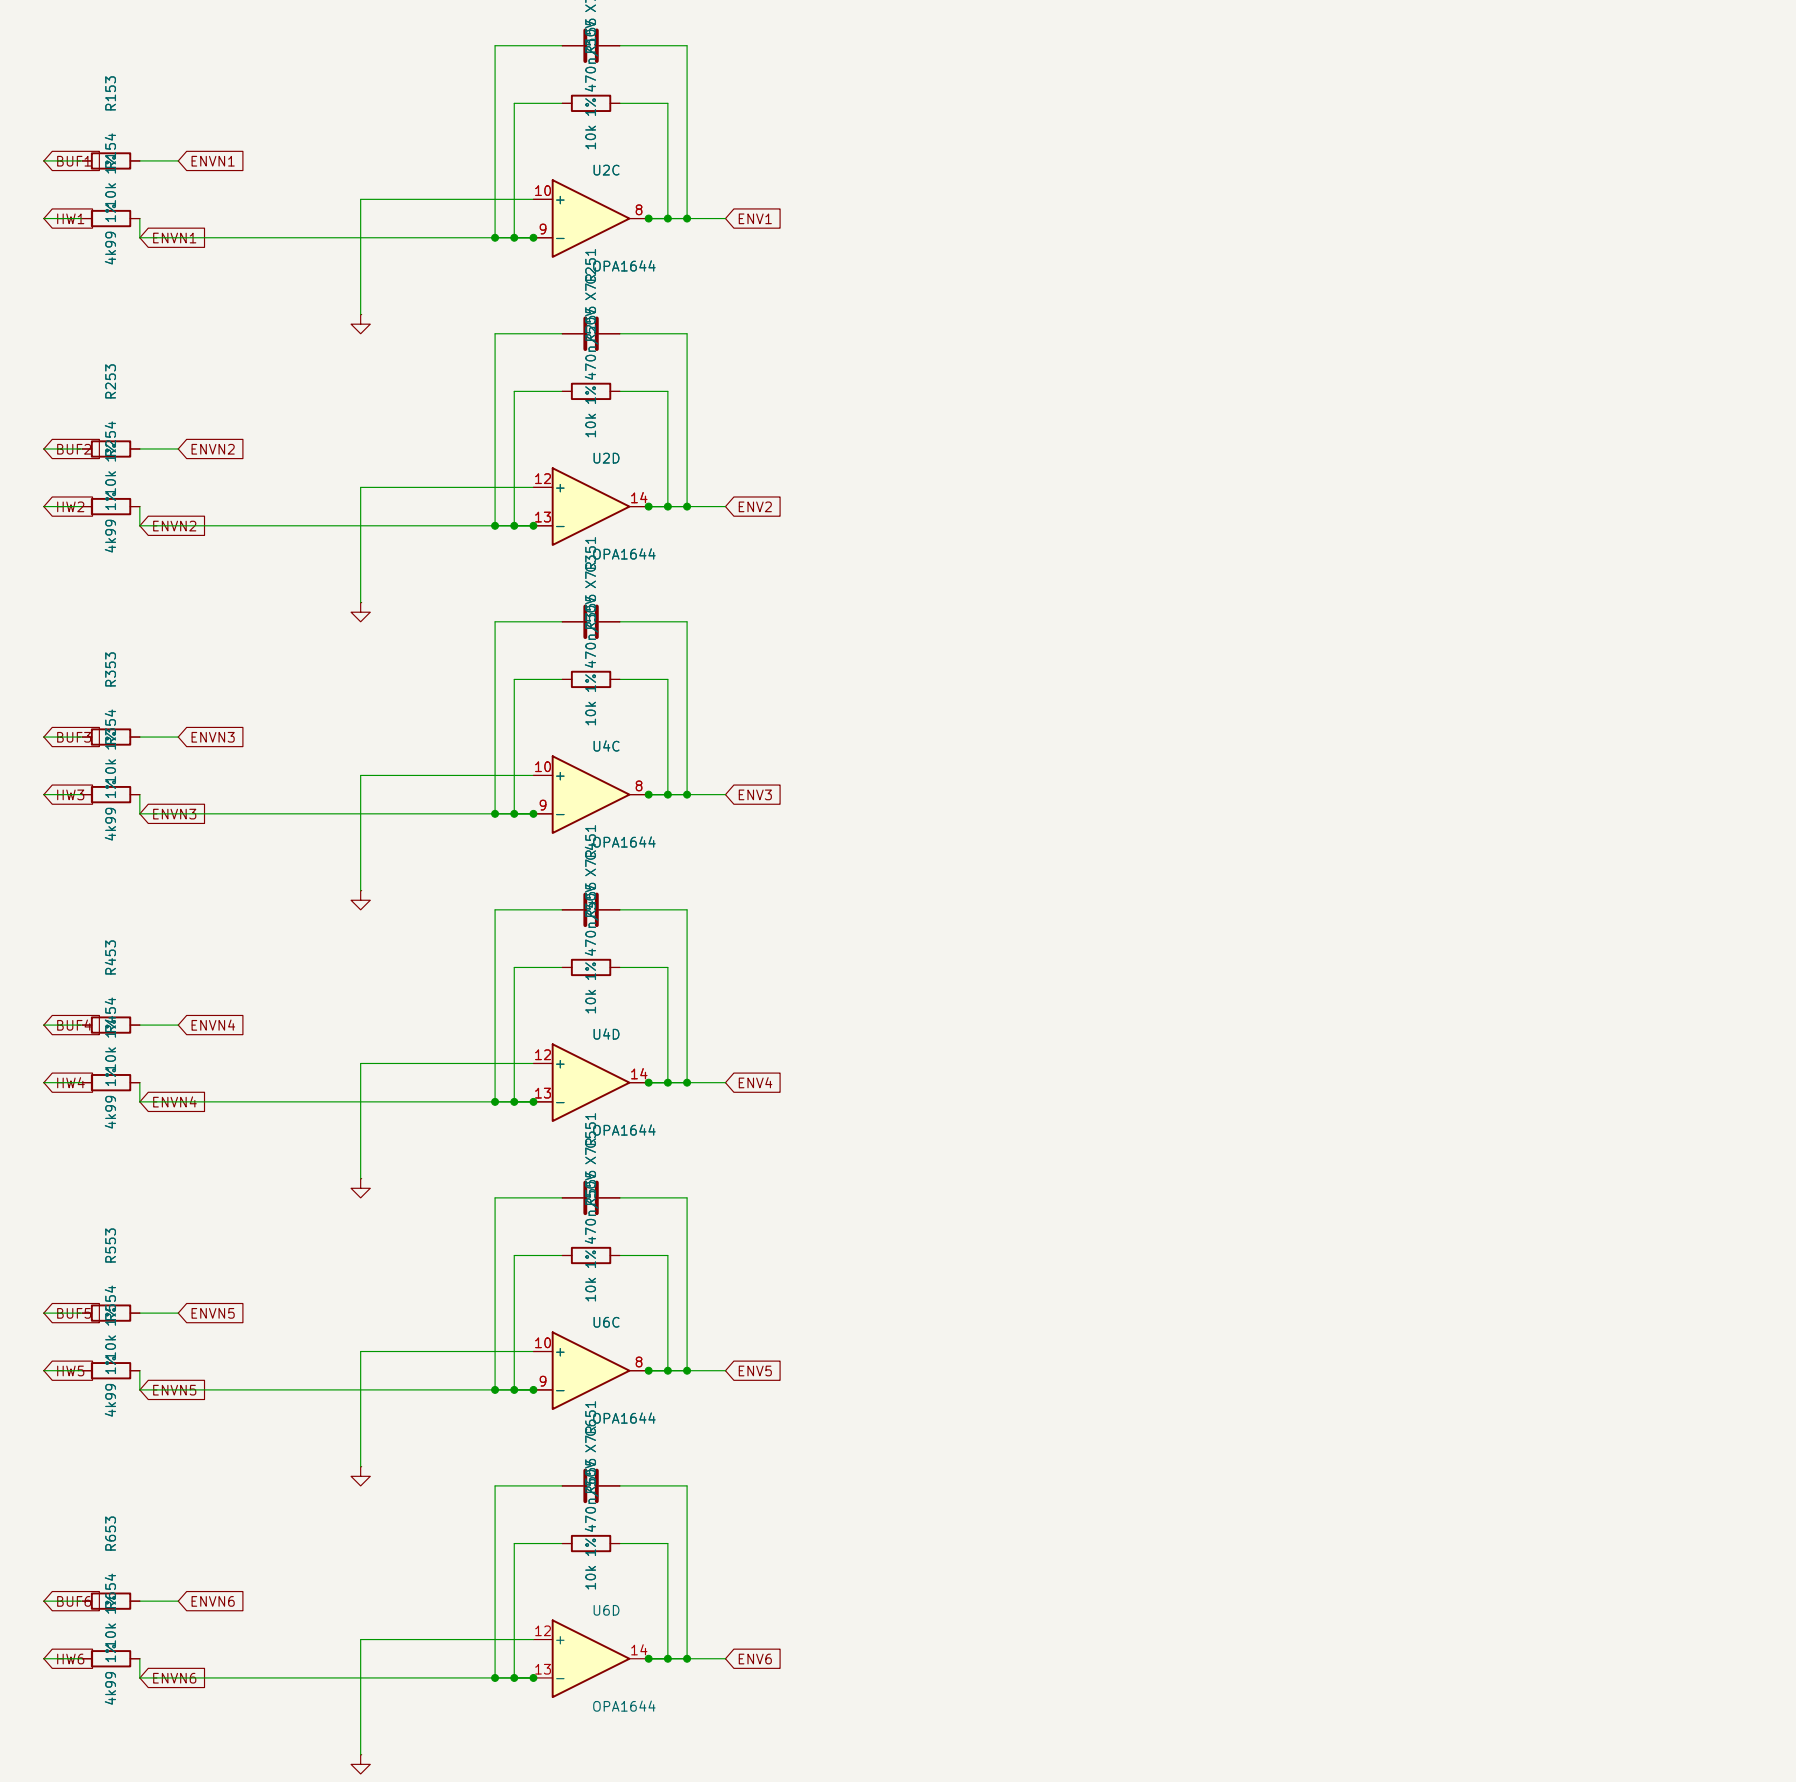
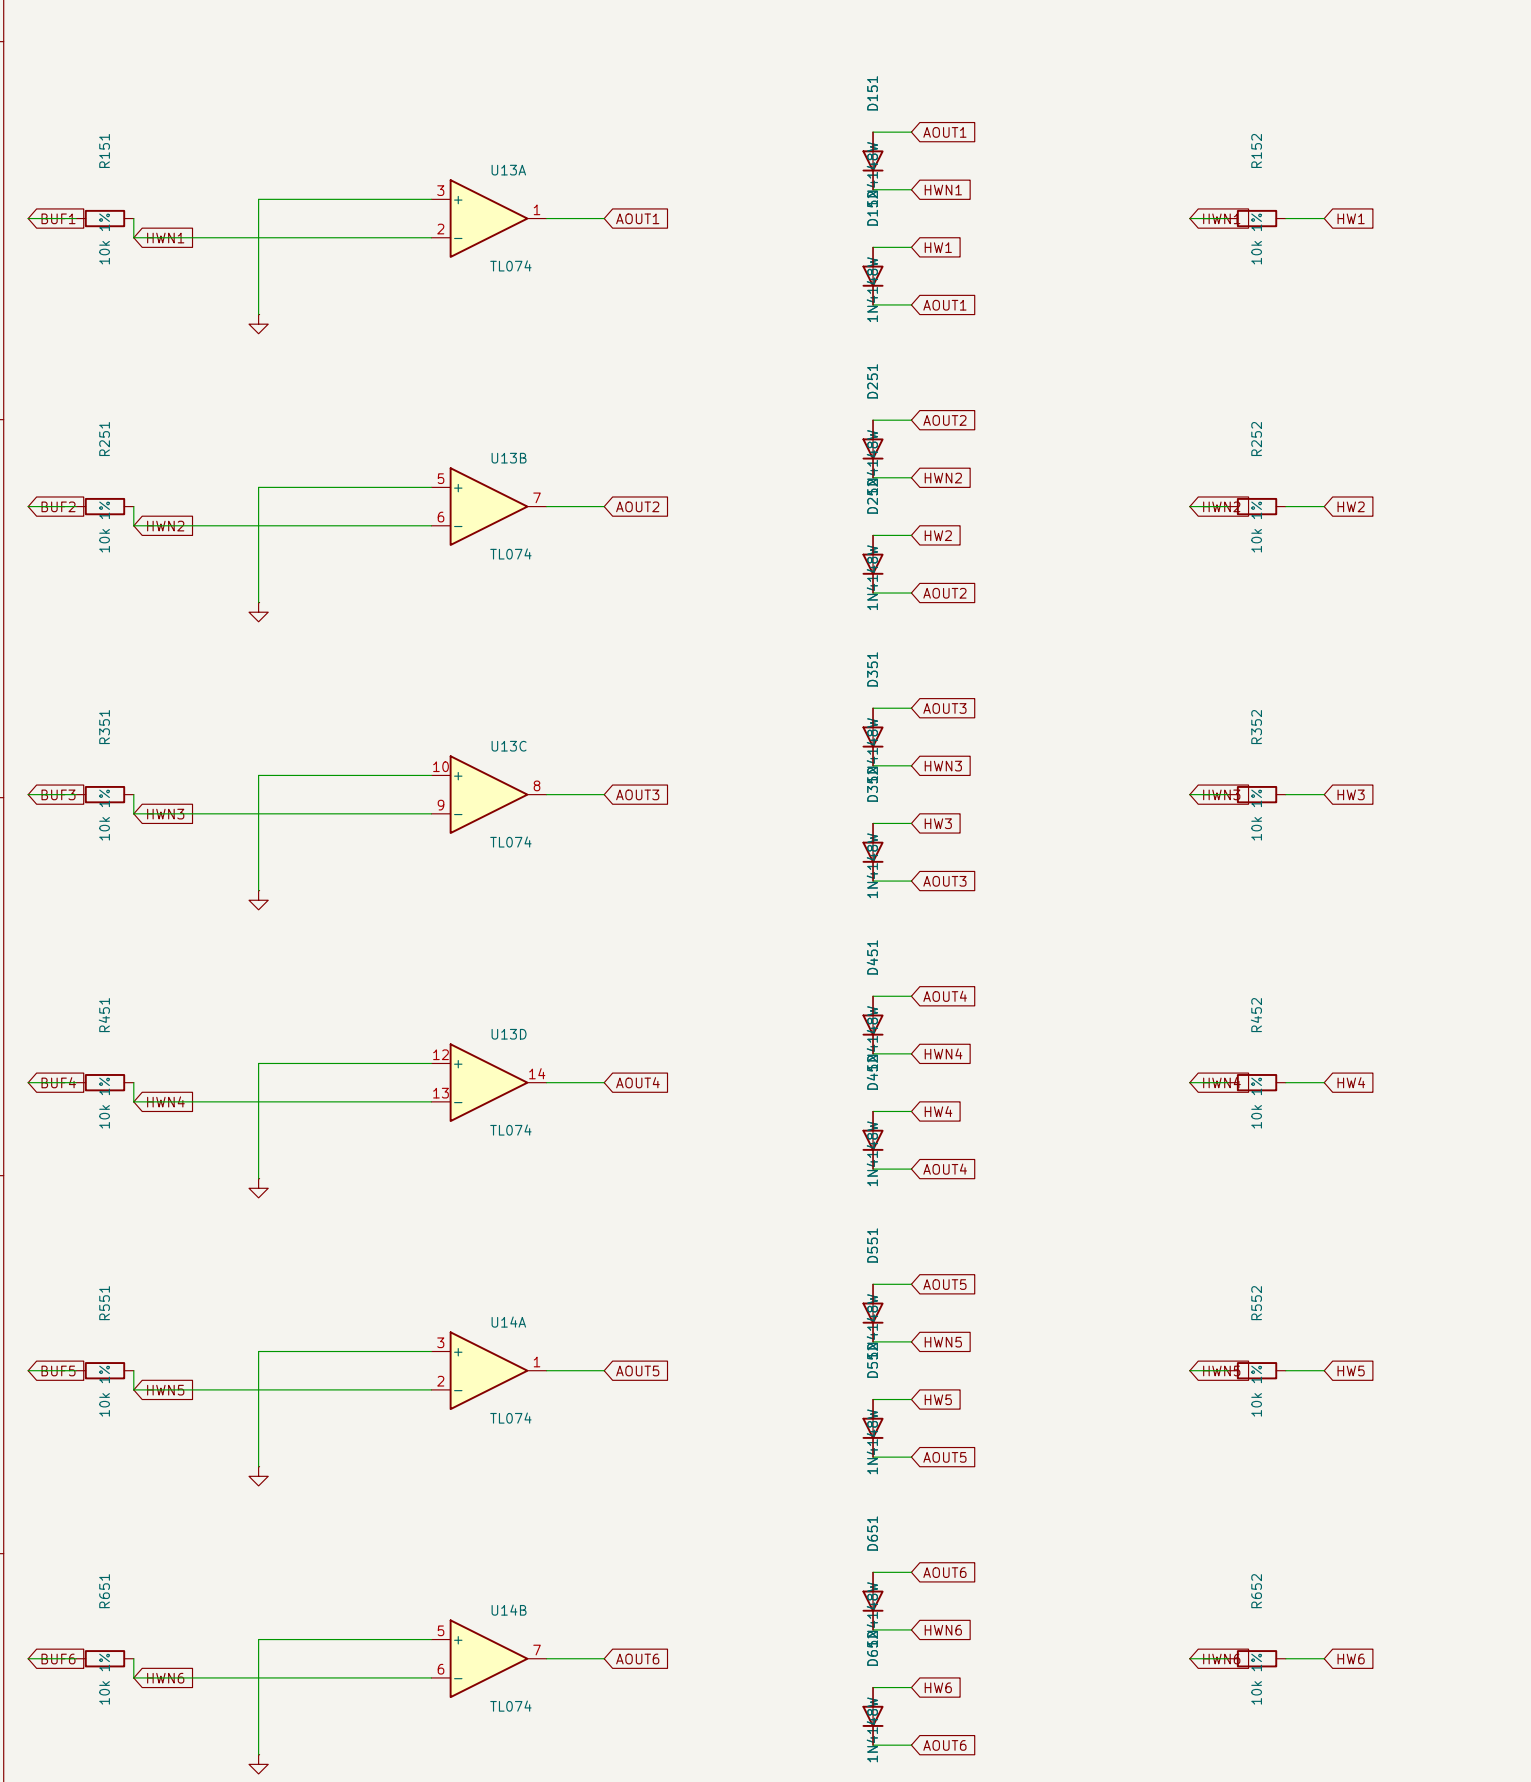
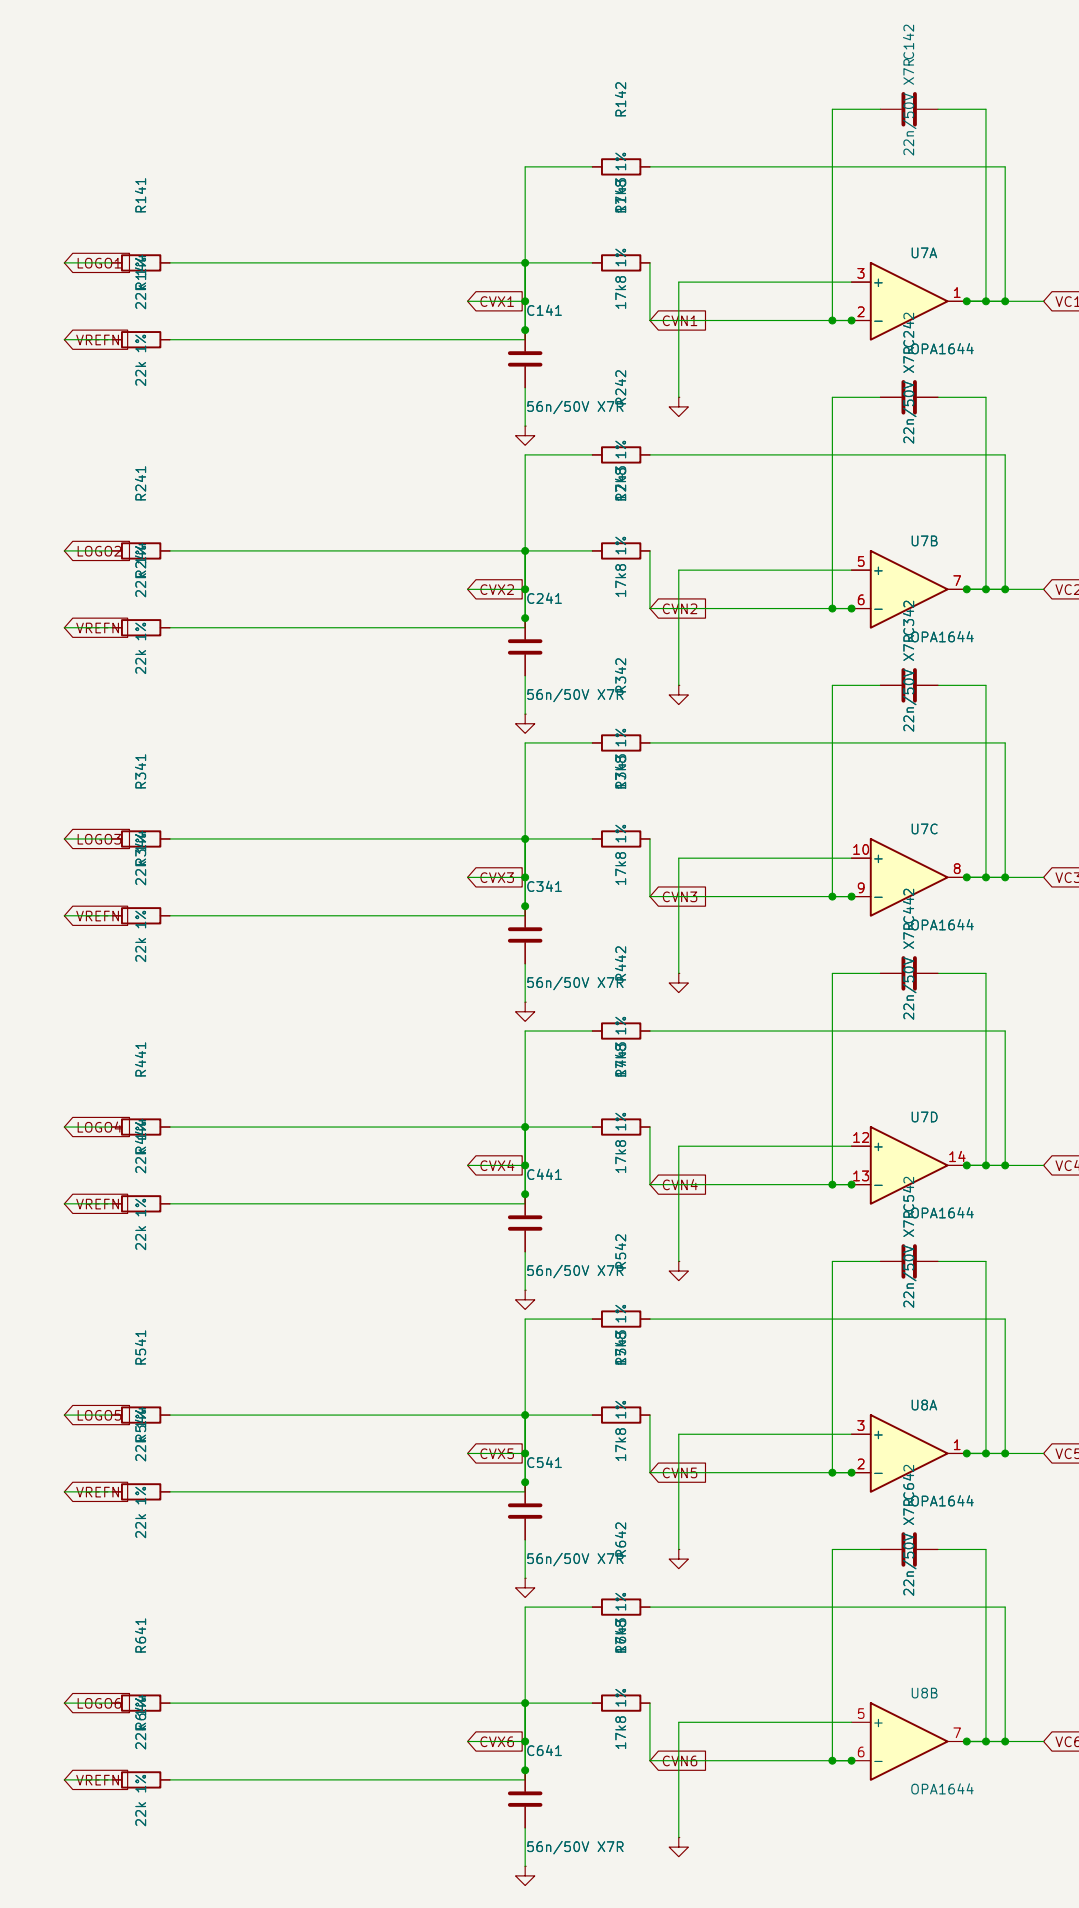


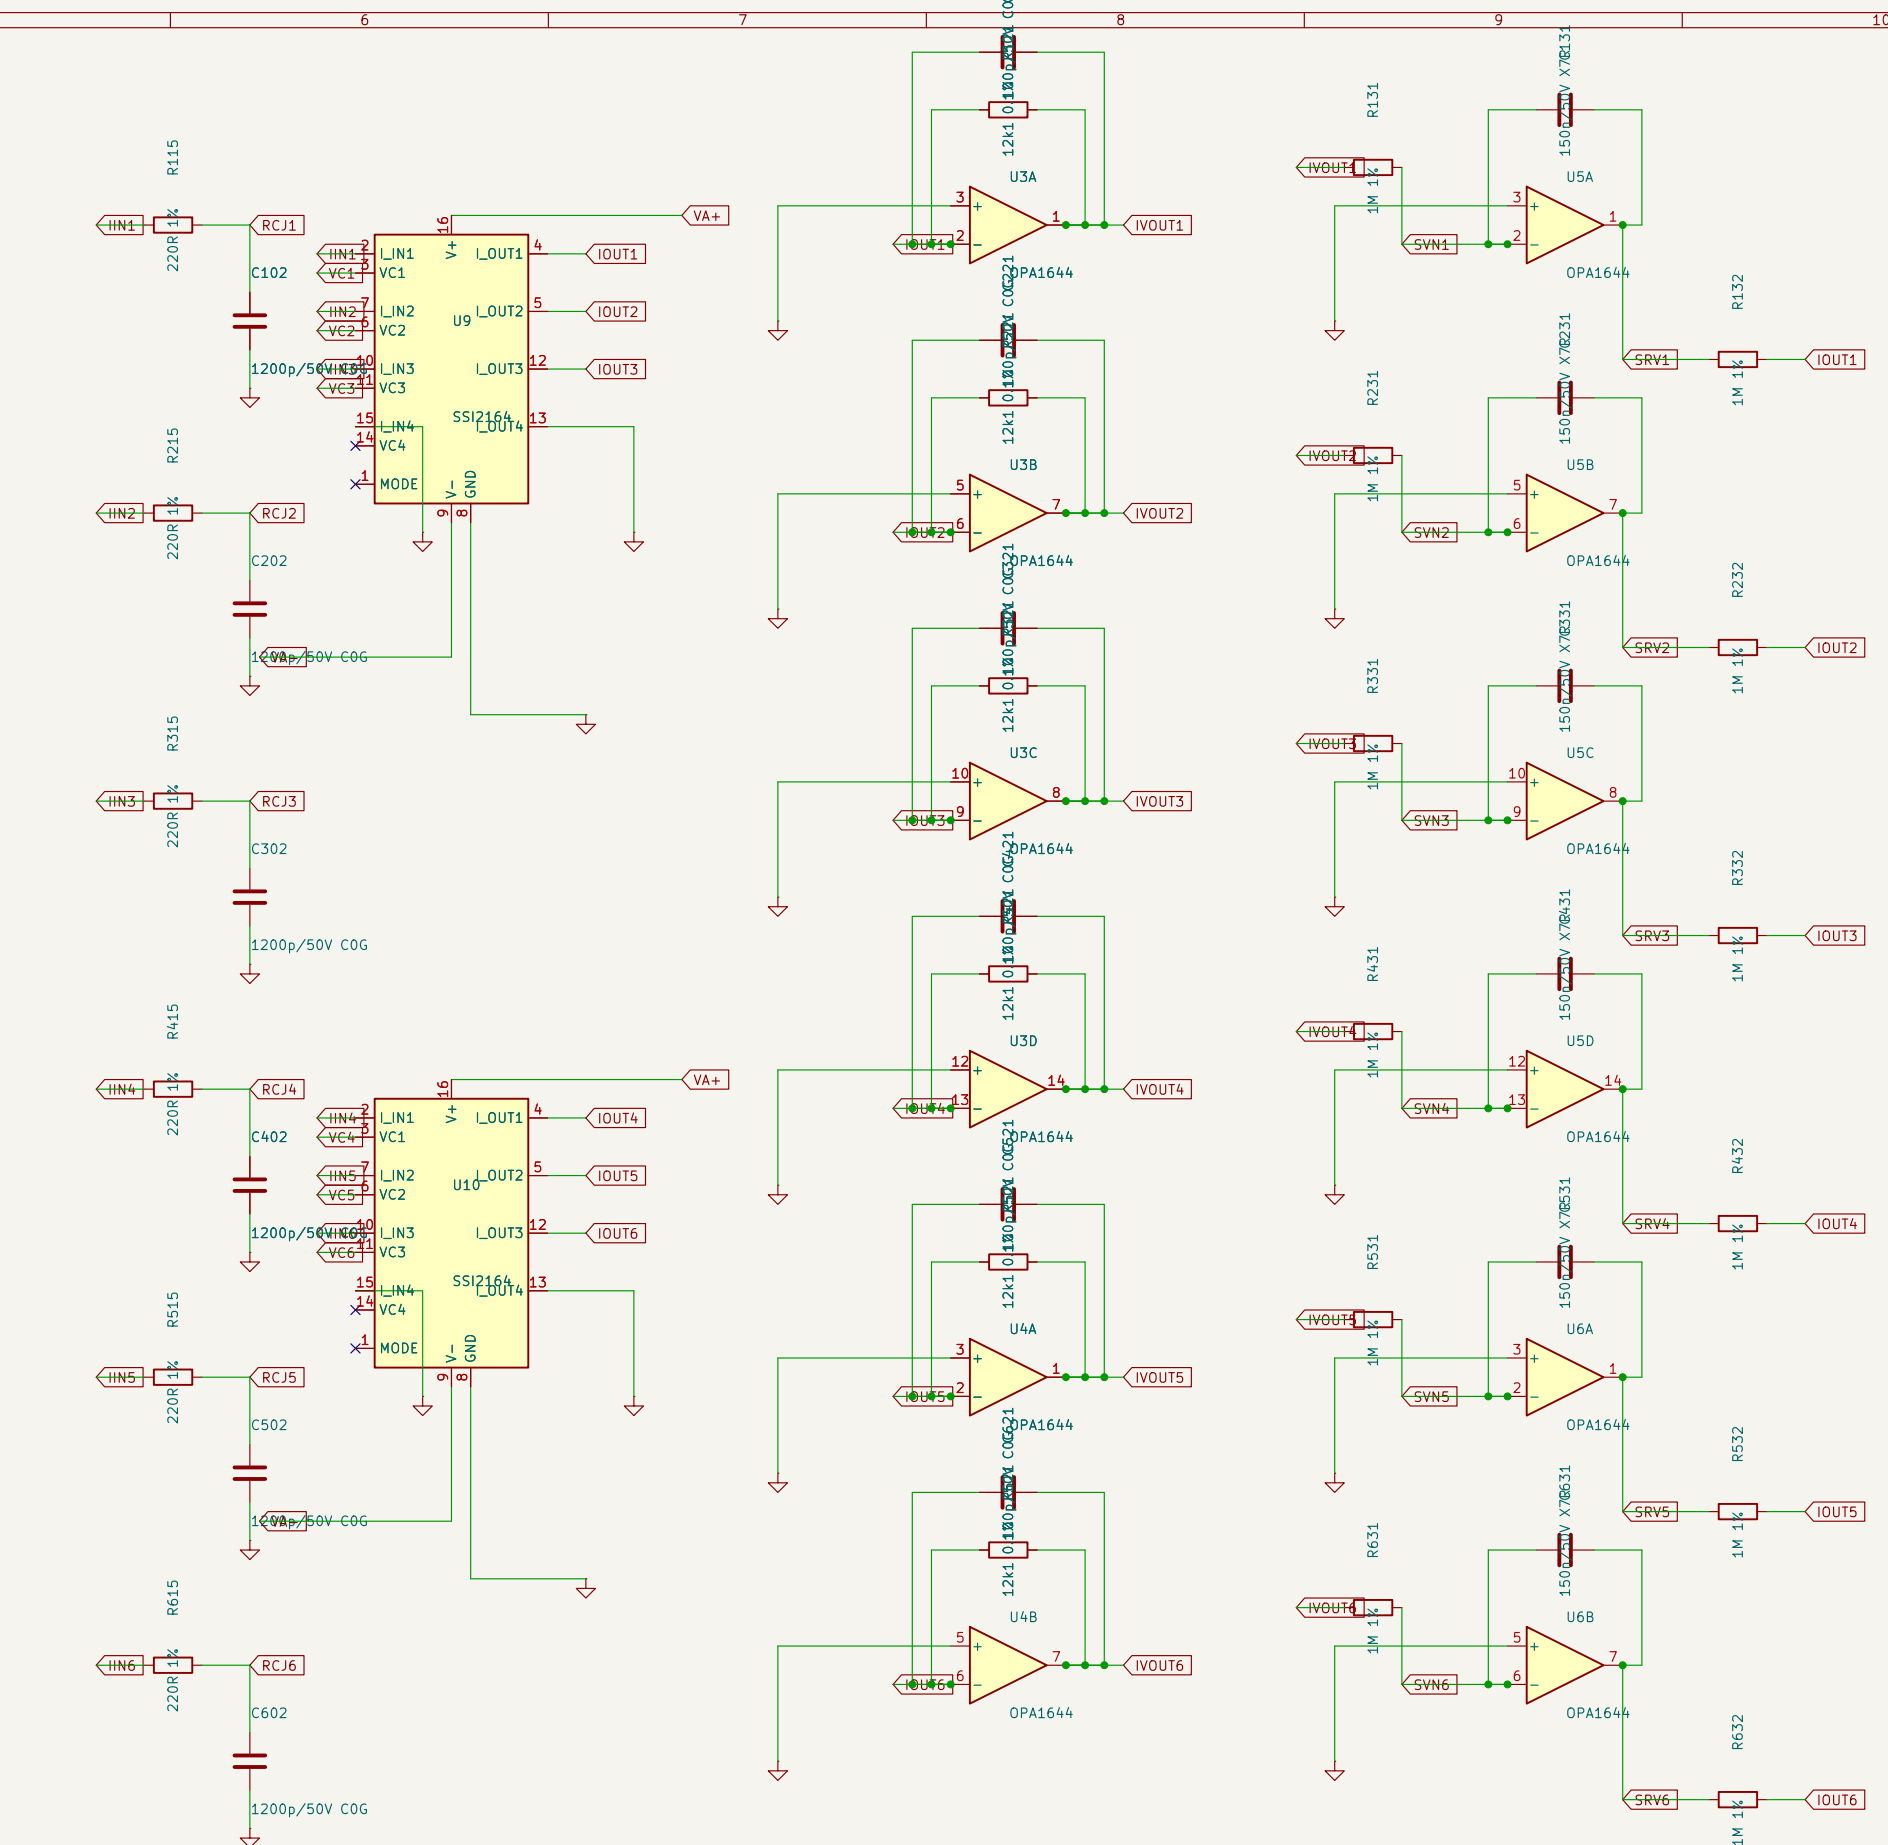

The boundary runs through U11: A-side from the digital domain, Y-side precision analogue, GND on MAGND. See floorplan.py.

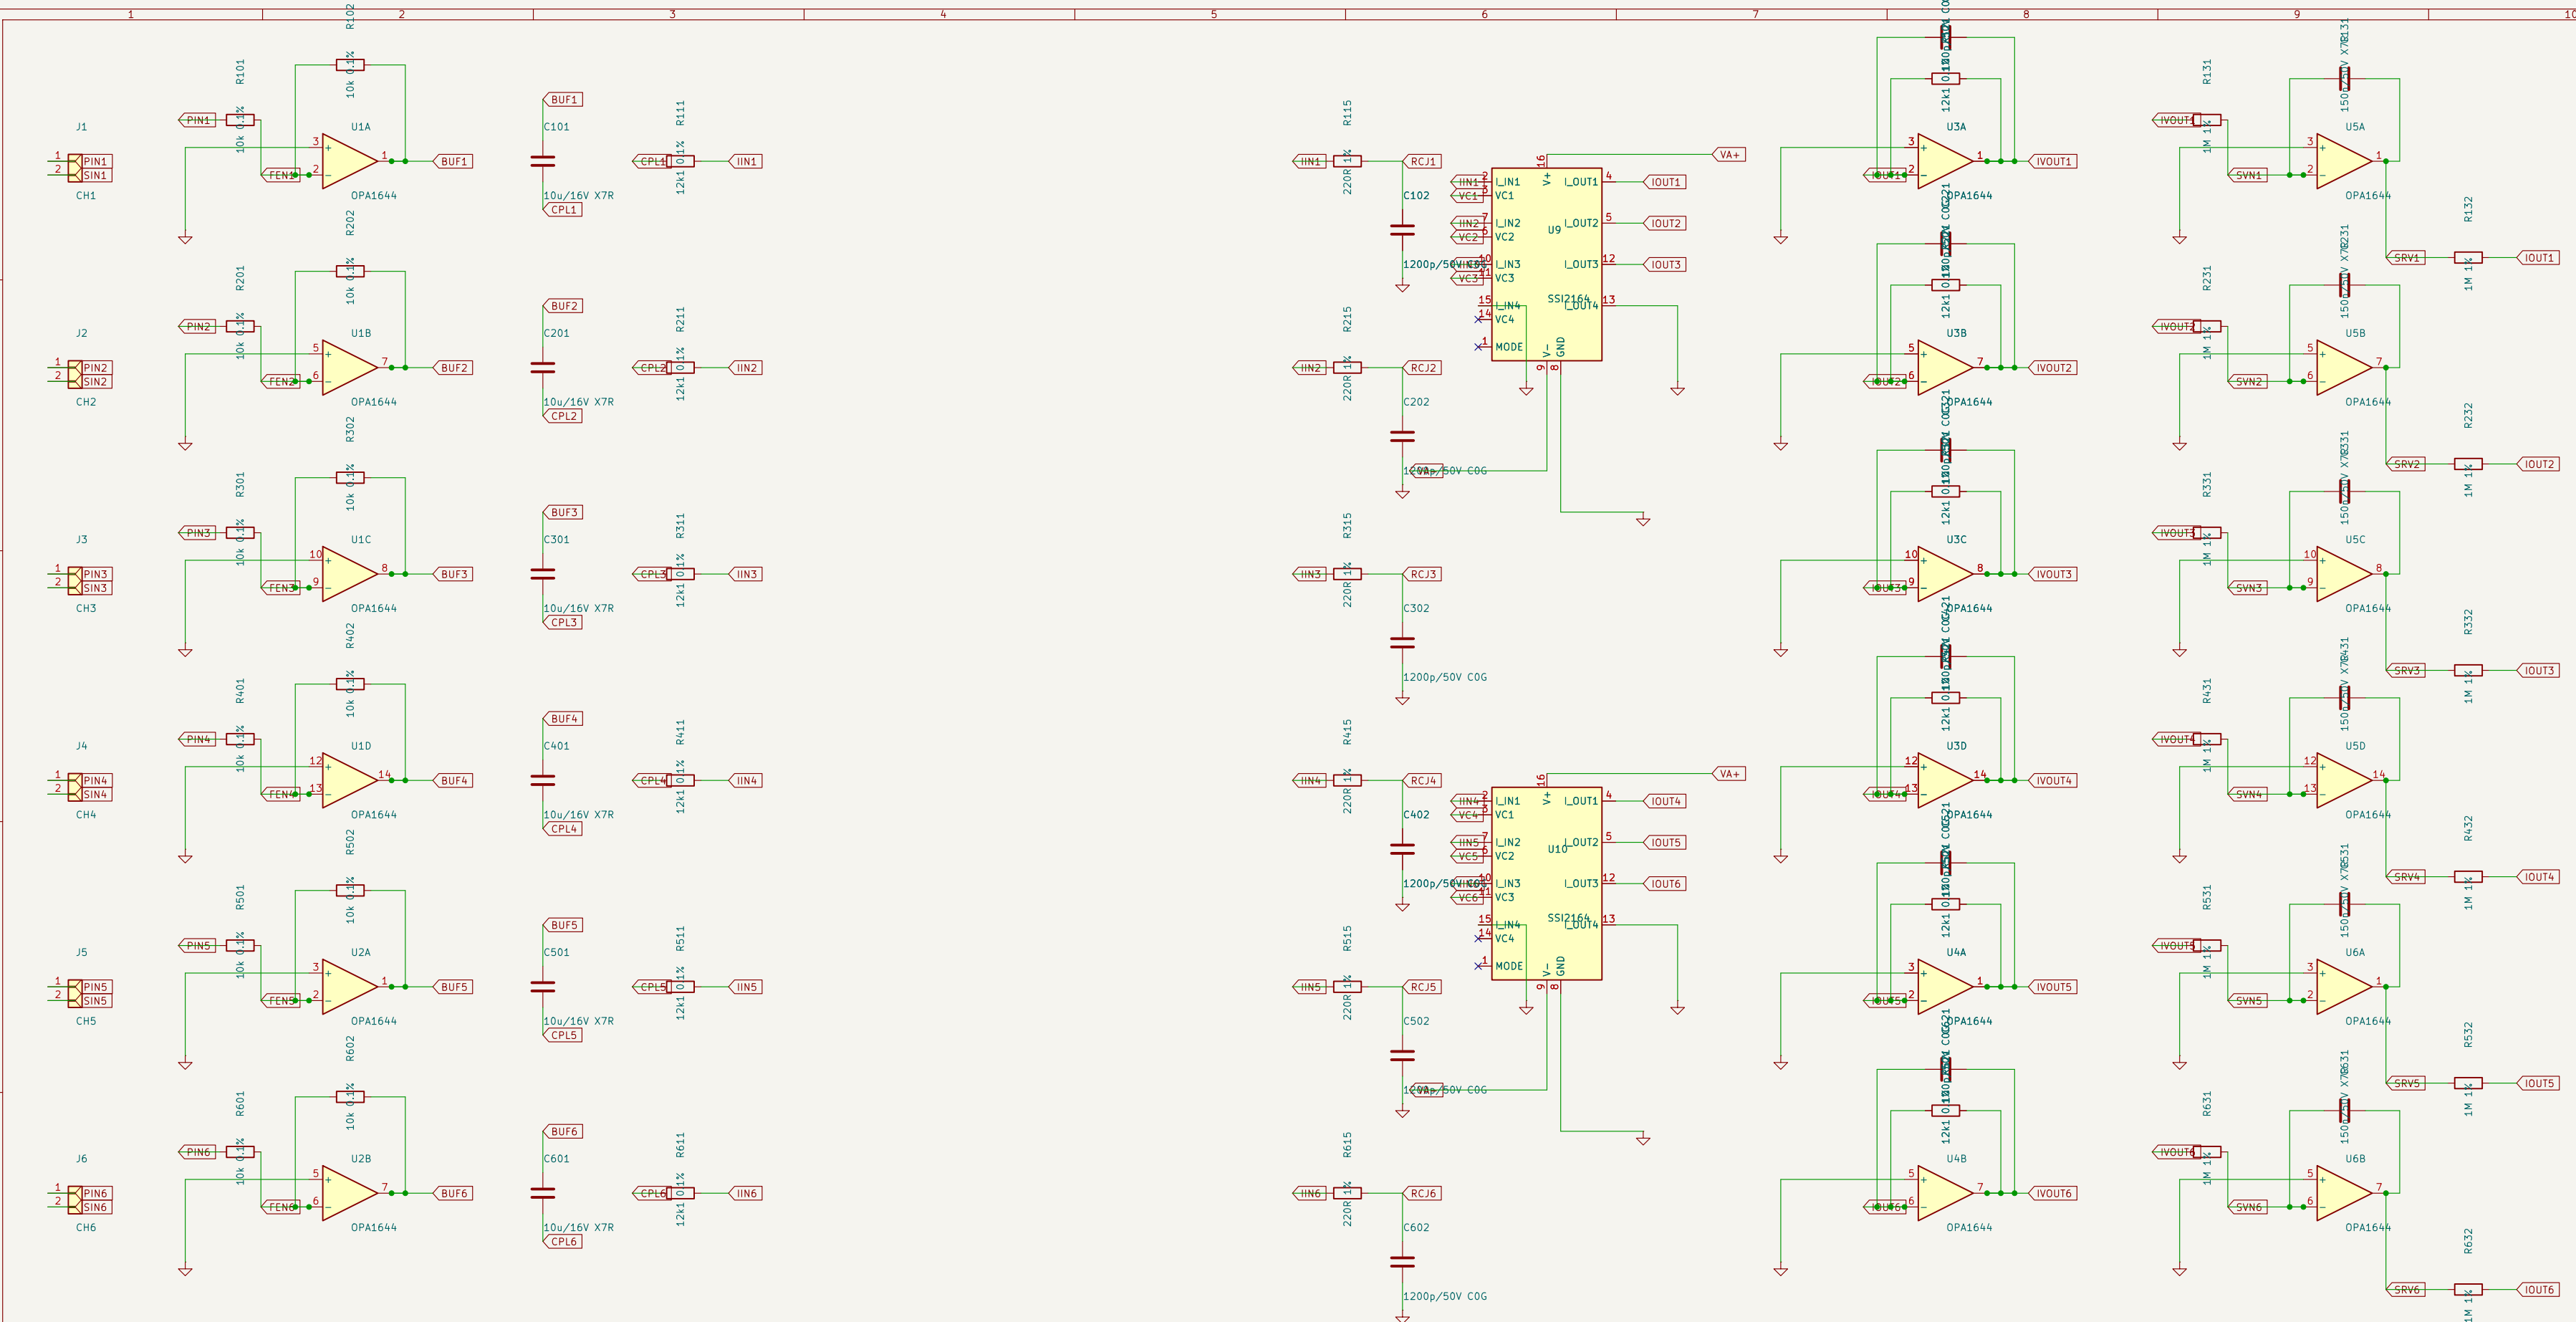